


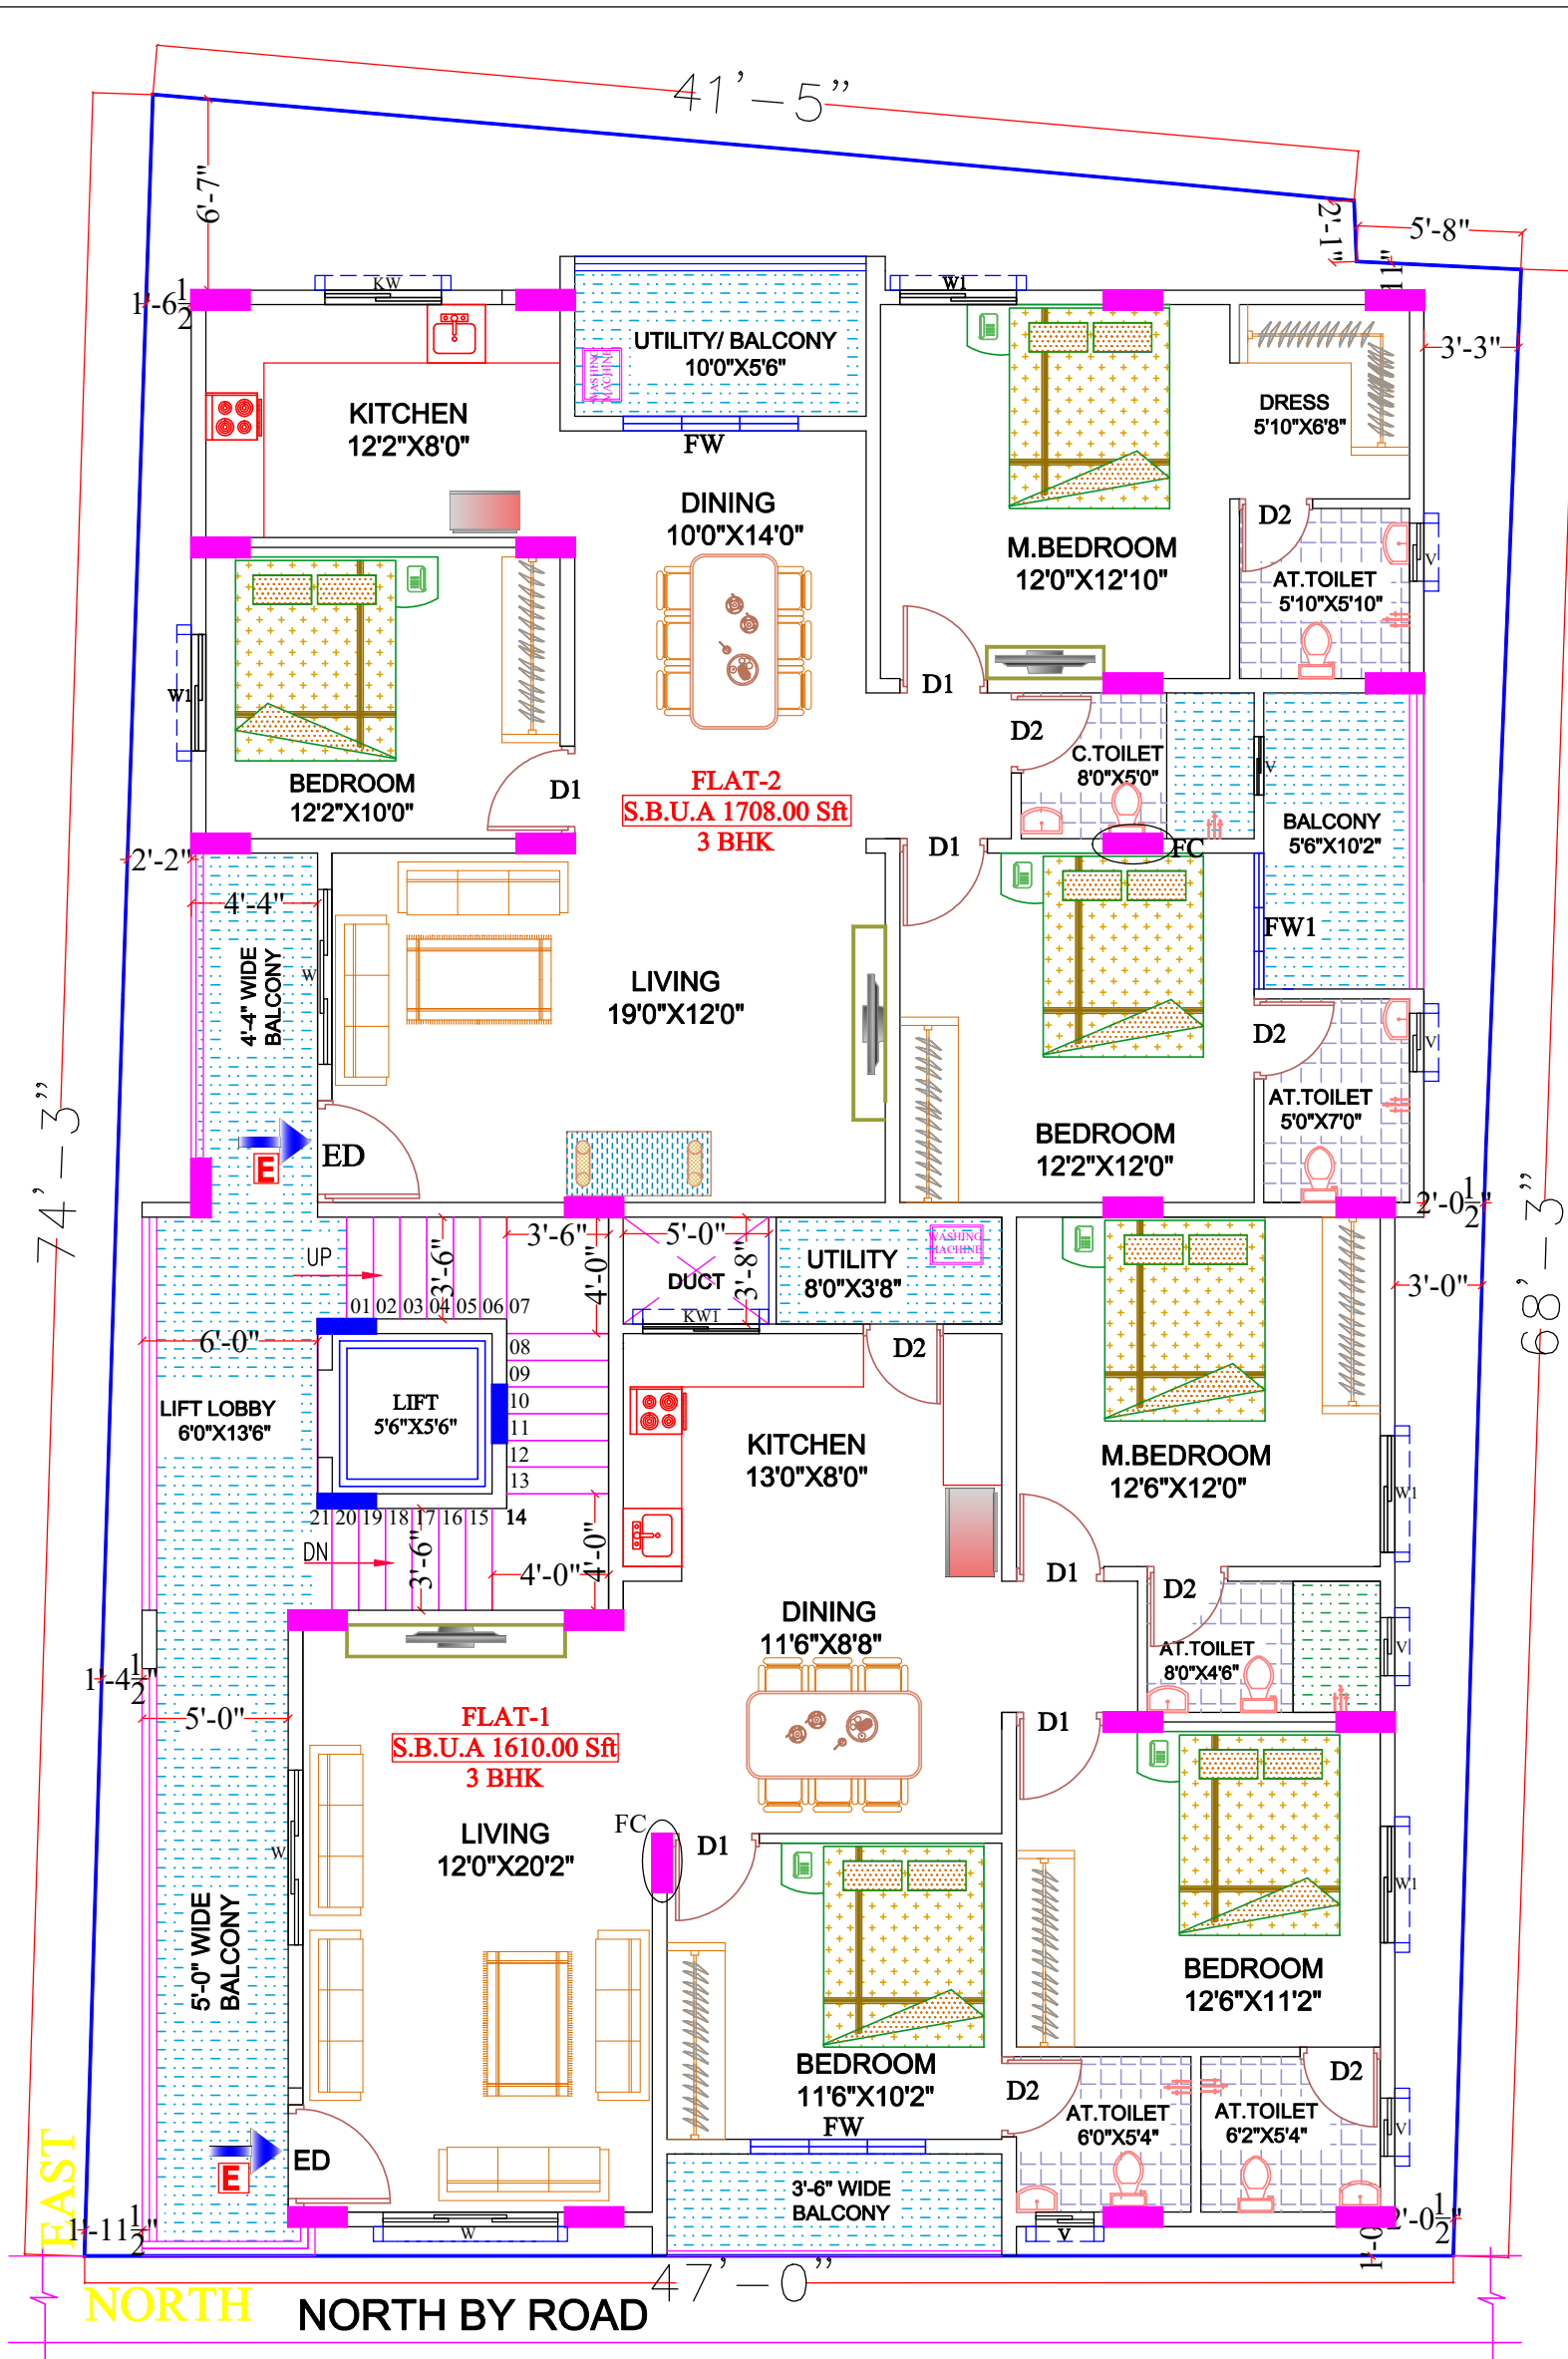

SCHEDULE OF OPENINGS		
TYPICAL FLOOR PLAN		
LINTEL HEIGHT -7'-0"		
DOOR		SIZES
ENTRENCE DOOR	ED	3'6"X7'0"
ROOM	D1	3'0"X7'0"
TOILET/ UTILITY	D2	2'9"X7'0"
FRENCH WINDOW DINING/ROOM	FW	6'0"X7'0"
	FW1	4'8"X7'0"
WINDOWS & VENTILATORS		
HALL WINDOW	W	6'0"X4'0"
ROOM WINDOW	W1	4'0"X4'0"
KITCHEN WINDOW	KW	4'0"X3'0"
VENTILATOR	V	2'0"X2'0"



CLIENT 'S

M/S. PRIME VISION

TITLE

SCHEME DRAWING

PROJECT

PROPOSED RESIDENTIAL APARTMENT AT BABANAGAR BENGALURU.

DATE: 20-08-2025

DEALT BY :HEMA/ APOORVA

SCALE: NTS

CKD BY: TNP

PAPANNA ASSOCIATES

ARCHITECT'S AND ENGINEERS

NO .230, FIRST FLOOR

YAJMAN BUILDING,

4TH MAIN ROAD, CHAMARAJPET, BANGALORE.

MOBILE NO -9845698929

email:papanna.associates@yahoo.com

papanna.associates17@gmail.com

TYPICAL FLOOR PLAN